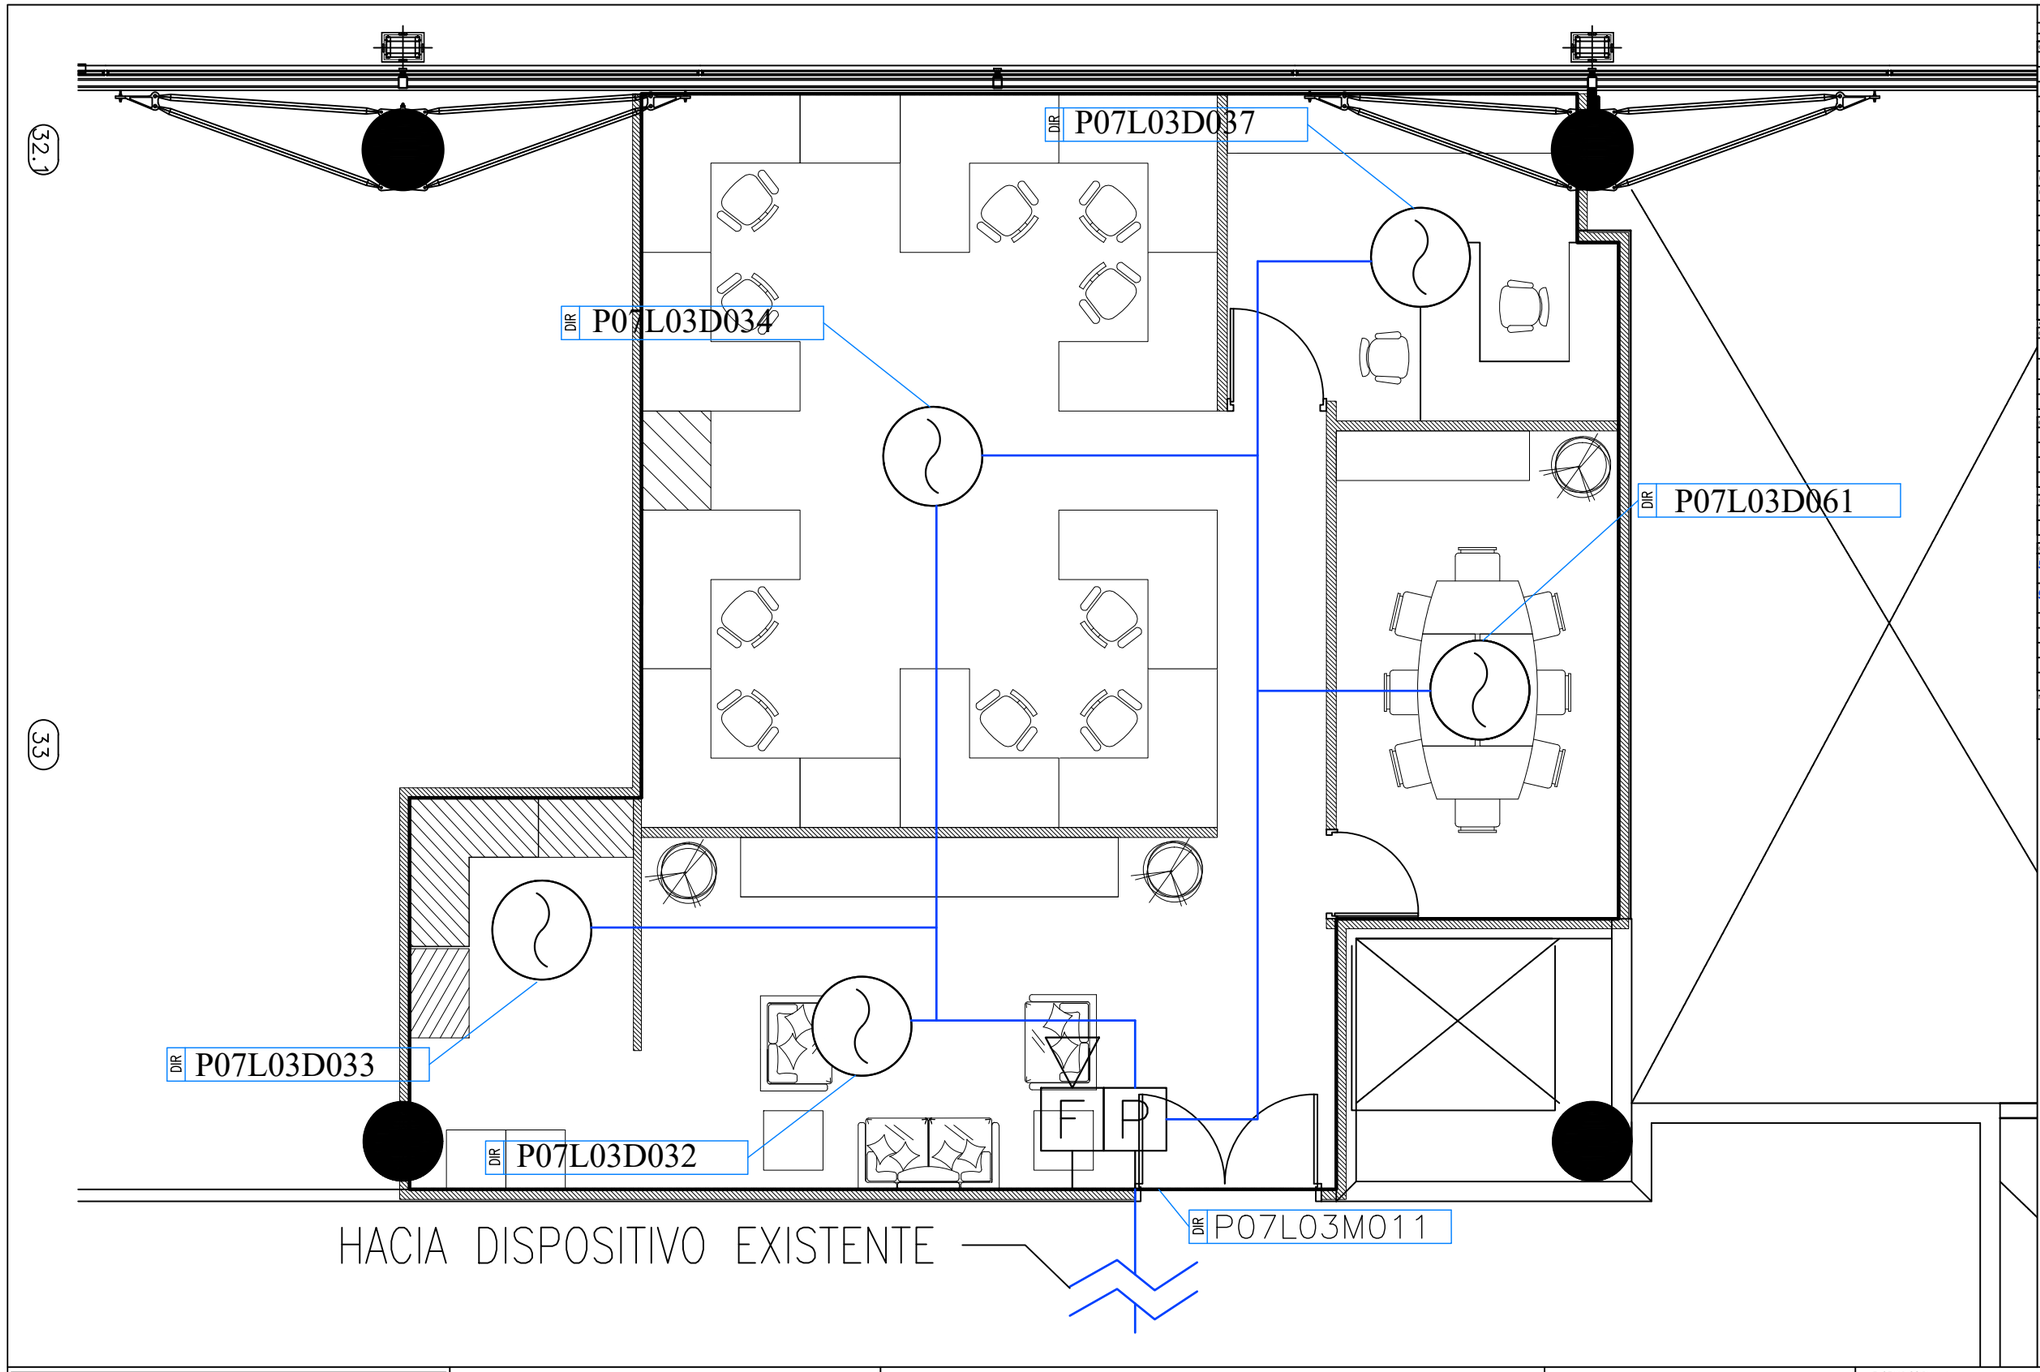

LEYENDA:

CONVENCIONES SISTEMA FADS

DISPOSITIVOS DE CAMPO DIRECCIONABLES

CONVENCIÓN	NOTACIÓN	DESCRIPCIÓN	MONTAJE
	S	Detector de humo con base estandar	TECHO
	S	Detector de humo con base estandar	MURO
	SI	Detector de humo con base aisladora	TECHO
	H	Detector térmico con base estandar	TECHO
	HI	Detector térmico con base aisladora	TECHO
	HR	Detector térmico (rate of rise) con base estandar	TECHO
	FD	Detector de llama	MURO
	SA	Detector de humo con housing para ducto	DUCTO
	B	Detector de humo por rayo proyectable, multimontaje	MURO TECHO
	BL	Detector de humo por rayo proyectable, multimontaje, largo alcance	MURO TECHO
	P	Estación Manual con stopper para interiores	MURO
	PE	Estación Manual con stopper para exteriores	MURO
	I	Módulo de Aislamiento	TECHO
	I	Módulo de Aislamiento	MURO
	R	Módulo de Relevo	MURO TECHO
	M	Módulo Monitor	MURO TECHO
	M	Módulo Control	MURO
	MT	Módulo para telefono bomberos	MURO TECHO

CONVENCIONES - FADS - DISPOSITIVOS DE CAMPO NOTIFICADORES

CONVENCIÓN	NOTACIÓN	DESCRIPCIÓN	MONTAJE
	SE	Sirena / Estrobo, muro, 15cd-115cd, color rojo	MURO
	SEE	Sirena / Estrobo, muro, 15cd-115cd, color rojo, exteriores	MURO
	E	Estrobo, muro, 15cd-115cd, color rojo	MURO
	EC	Estrobo, techo, 15cd-115cd, color rojo	TECHO

CONVENCIONES - FADS / PANELES Y EQUIPOS PERIFERICOS

CONVENCIÓN	NOTACIÓN	DESCRIPCIÓN	MONTAJE
FACP	FACP	Panel de detección y alarma de incendio	MURO
FAPA	FAPA	Panel anunciador de red	MURO
DAA	DAA	Amplificador de audio digital	MURO
FAP	AP	Fuente de alimentación auxiliar	MURO

CONVENCIONES - FADS / OTROS

CONVENCIÓN	NOTACIÓN	DESCRIPCIÓN	MONTAJE
	T	Telefono Bomberos	MURO
	TIC	Estación Combinada	MURO

CONVENCIONES - FADS / TUBERIA

CONVENCIÓN	NOTACIÓN	DESCRIPCIÓN
	N/A	Tuberia bajando: Azul: Direccionadores Rojo: Notificacion Magenta: Telefonos
	N/A	Tuberia subiendo: Azul: Direccionadores Rojo: Notificacion Magenta: Telefonos
	N/A	Tuberia Direccionadores
	N/A	Tuberia Notificadores
	N/A	Tuberia Telefonos
	N/A	Trayectoria detectores de rayo proyectado
	N/A	Tuberia Fibra optica 6H

Nota: la tuberia total utilizada en el sistema FADS es de tipo Ø 3/4" EMT (con marcaciones en color ROJO cada 3mts.)

	N/A	Numero de cables: Azul: Direccionadores (Belden # 16) Rojo: Notificacion (Belden # 16) Magenta: Telefonos (Belden # 16)

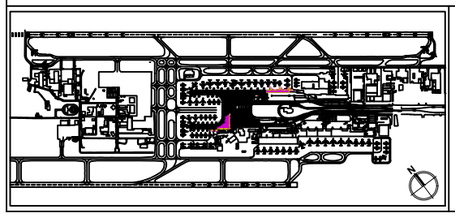

OPAIN S.A.
Concesionario Aeropuerto Internacional Eldorado

Johnson Controls

		FIRMA	FECHA
DISEÑADO, SUMINISTRADO O CONSTRUIDO POR :	EMPRESA JOHNSON CONTROLS	Andres Gutierrez	21/02/2025
VERIFICADO POR :	OPAIN S.A. DIRECCIÓN DE INGENIERIA Y ARQUITECTURA		
APROBADO POR :	OPAIN S.A. DIRECCIÓN DE INGENIERIA Y ARQUITECTURA		

EL DORADO

PROYECTO DE MODERNIZACION Y EXPANSION DEL AEROPUERTO EL DORADO, EN LA CIUDAD DE BOGOTA D.C.
Sociedad Concesionaria Operadora Aeroportuaria Internacional S.A
OPAIN S.A.

REVISIÓN Y CONTROL DE VERSIONES

REV.	FECHA	MODIFICACIÓN	ESTADO
1	ASBUILT	25-03-2025	
A	11-02-2025	DISEÑO	

FASE Y DISCIPLINA :
FASE 4 – PLANOS ASBUILT
ARQUITECTURA

TÍTULO :
Nuevo Edificio Terminal Unificado de Pasajeros
OFICINAS AEROCIVIL
SISTEMA – FADS
MUELLE INTERNACIONAL SUR – NIVEL 4.70

NÚMERO DE CONTRATO	NÚMERO DE DIBUJO	REV.	ESCALA (B1)
	EST-GAA12800-YF1-01	1	IND